



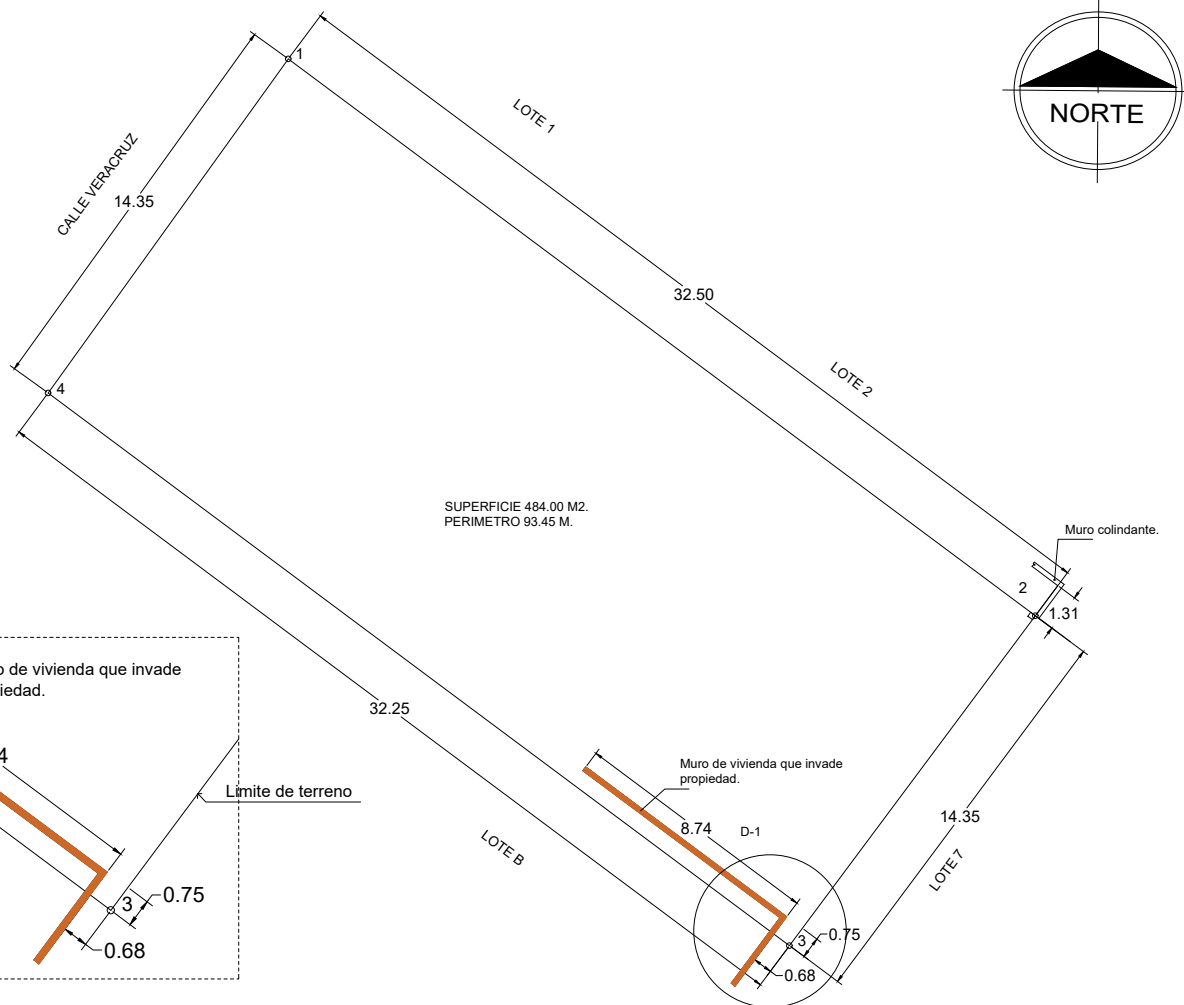

LOCALIZACIÓN

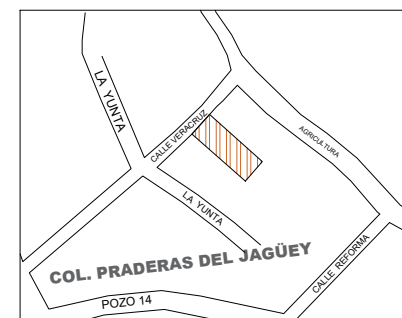

UBICACIÓN SATELITAL: 17° 58' 31.987795 N 94° 34' 6.355802 W

INCIDENCIAS:

- SE REALIZA LA MEDIDA DEL VERTICE 1 CON VERTICE 2 Y EFECTIVAMENTE SE CORROBORO LA DISTANCIA DE 32.50 MTS.
- SE TOMO LA MEDIDA CON RESPECTO AL VERTICE 2 Y VERTICE 3 Y SE MUESTRA UNA MOJONERA EXISTENTE DE CONCRETO ARMADO EN V-2. DATOS EMITIDOS POR EL VECINO DEL LOTE 7 (POSTERIOR.) AL REALIZAR LA MEDIDA CON RESPECTO AL VERTICE -2 CON VERTICE-3 Y SE VISUALIZA QUE EXISTE UNA INVASIÓN DE UN MURO DEL LOTE 8, EXISTENTE EN 0.75 MT.(75 CMS).POR 8.74MTS CON RESPECTO A ESA MISMA COLINDANCIA LADO SUROESTE.SE COLOCA MOJONERA CON UNA VARILLA DE 3/4" DIAM. DEJANDO UNA MOJONERA CON VARILLA DE MEDIA Y CONCRETO A UNA DISTANCIA DEL V-3 CON V-4 EN 32.25 MTS.
- QUEDANDO UNA MOJONERA EN V-3 CON UNA DISTANCIA DE 14.35 MTS CON V-1.
- QUEDA ASENTADO EN ESTE DOCUMENTO PARA CUALQUIER DUDA O ACLARACIÓN.

SUPERFICIE 484.00 M2.
PERIMETRO 93.45 M.
COLINDANCIAS:

- AL NORESTE EN 32.50 M. CON LOTES 1-2
AL SUROESTE EN 32.25 M. CON LOTES 8
AL SURESTE EN 14.35 M. CON LOTES 7
AL NOROESTE EN 14.35 M. CON CALLE VERACRUZ.

CUADRO DE CONSTRUCCIÓN

LADO ESTACIÓN P.V.	AZIMUT	DISTANCIA (MTS)	COORDENADAS UTM ESTE (X) NORTE (Y)		CONVERGENCIA	FACTOR DE ESCALA LINEAL	LATITUD	LONGITUD
1 - 2	134° 56' 16.53"	32.50	333,925.62	1988,193.07	-0° 29' 2.900415"	0.99994100	17° 58' 32.336617 N	94° 34' 6.231928 W
2 - 3	223° 5' 21.65"	14.35	333,946.62	1988,170.11	-0° 29' 2.637617"	0.99994090	17° 58' 31.596450 N	94° 34' 5.443393 W
3 - 4	314° 57' 22.10"	32.25	333,936.62	1988,159.64	-0° 29' 2.730639"	0.99994094	17° 58' 31.252885 N	94° 34' 5.773577 W
4 - 1	42° 5' 25.08"	14.35	333,916.00	1988,182.42	-0° 29' 2.991346"	0.99994104	17° 58' 31.987795 N	94° 34' 6.355802 W

TIPO DE OBRA:

PLANO QUE AMPARA EL DERECHO DE PROPIEDAD.

PROPIETARIO: C. PORFIRIO PALOMEC CANDELARIA.	PERITO DE OBRA: ARG. JOSÉ MANUEL CONTRERAS GLEZ.
UBICACIÓN: CALLE VERACRUZ No. 10 COL. PRADERAS DEL JAGÜEY MINATITLÁN, VER.	CEDULA PROFESIONAL 1679326 PERITO DRO # 036 DR SSV No. 11-SSV-047/2007

TIPO DE PLANO:
PLANTA DE TERRENO Y COLINDANCIAS.

DIGITALIZO:
ARG. JOSÉ MANUEL CONTRERAS GONZÁLEZ

ACOTACIÓN:
METROS

FECHA:
ENERO / 2023.

ESCALA:
1:100

PLANO No.
MD-01