


FACHADA PRINCIPAL DE ACCESO

escala 1:50



FACHADA PRINCIPAL DE ACCESO


escala 1:50

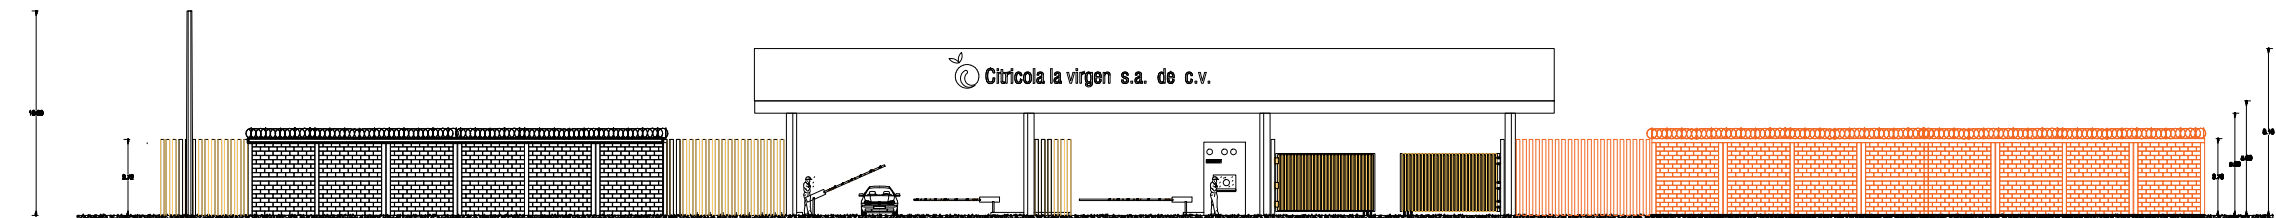

FACHADA PRINCIPAL DE BARDA PERIMETRAL

escala 1:50

LOCALIZACIÓN

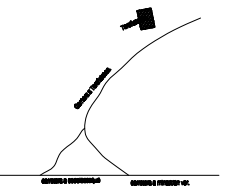

ESPECIFICACIONES GENERALES.

CIMENTACIONES
LA CIMENTACION DEBERA SE DESPLANTARSE SOBRE TERRENO
NATURAL CON RESISTENCIA MINIMA DE 8T/M2

ACEROS

BARRA	DIAMETROS	BARRA	DIAMETROS	BARRA	DIAMETROS
2	1/4 "	3	3/8 "	4	1/2 "
5	5/8 "	6	3/4 "		


ACERO DE REFUERZO $f_y = 4200 \text{ KG/CM}^2$ ASTM. A-615

ACERO EN ESTRIBOS $f_y = 2530 \text{ KG/CM}^2$ ASTM. A-615

UNICAMENTE EN ACERO DEL NUMERO 2 (ALAMBREON)

LONGITUD MINIMA DE TRASLAPES Y GANCHOS.
PARA VARILLAS CON MAS DE 30CM DE CONCRETO POR DEBAJO DE
ELLAS, CASO CONTRARIO SE REDUCIRA DIVIDIENDO LOS VALORES
DE LA LISTA ENTRE 1.4 PERO NO MENOR DE 30CM.

3/8" $\phi = 30CM$ 1/2" $\phi = 35CM$ 5/8" $\phi = 50CM$

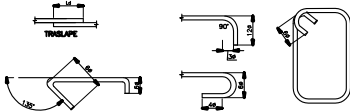

NOTAS GENERALES.

- 1.-ACOTACIONES EN CM, NIVELES EN MTS, EXCEPTO DONDE SE
INDIQUE OTRA UNIDAD.
- 2.-CONCRETO NORMAL EN CIMENTACION, TRABES, COLUMNAS Y LOSAS DE
 $f_c = 250 \text{ KG/CM}^2$, REVENIMIENTO DE 14CM. TAMAÑO MAXIMO DEL
AGREGADO 3/4" (19MM)
- 3.-CONCRETO EN DALAS Y CASTILLOS $f_c = 200 \text{ KG/CM}^2$ CEMENTO NORMAL
CON REVENIMIENTO DE 14 CM. TAMAÑO MAXIMO DE AGREGADO 3/4" (19MM)
- 4.-CONCRETO NORMAL EN PLANTILLAS DE $f_c = 100 \text{ KG/CM}^2$, REVENIMIENTO
REVENIMIENTO DE 14CM. TAMAÑO MAXIMO DE AGREGADO 3/4" (19MM)
- 5.-PARA COLAR USAR REVOLVEDORA Y VIBRADOR MECANICO
- 6.-CURAR EL CONCRETO POR CUALQUIER METODO DURANTE 5 DIAS
- 7.-TODAS LAS MEDIDAS DE LOS ELEMENTOS ESTRUCTURALES SON
SIN ACABADOS.
- 8.-RECUBRIMIENTO LIBRE EN CIMENTACION, 5CM., COLUMNAS 3CM Y
TRABES 3CM.
- 9.-LOS RECUBRIMIENTOS DEBERAN SER VERIFICADOS DURANTE LA
EJECUCION DE LA OBRA.
- 10.-TODOS LOS ELEMENTOS DEBERAN SER VERIFICADOS Y NIVELADOS DURANTE
Y DESPUES DEL COLODO PARA EVITAR DESPLACES POR VIBRACION
- 11.-MURO INTERIOR DE BLOCK HUECO DE 13X20X40CM JUNTADO CON
MORTERO CEMENTO ARENA 1:4 APLANADO FINO
- 12.-MURO DE BLOCK HUECO DE 10X20X40CM JUNTADO CON
MORTERO CEMENTO ARENA 1:4 PARA BARDAS Y PRETILES
- 13.-EL NIVEL +0.00 CORRESPONDE AL NIVEL DE BANQUETA DE LA
VIA PUBLICA DEL LUGAR DE LA OBRA.
- 14.-ANTES DE COLAR, VERIFICAR Y COLOCAR TODOS LOS SISTEMAS DE TUBERIA
Y DE INSTALACIONES EMBEBIDOS EN LA CIMENTACION.
- 15.-COMPACTAR EL RELLENO CON EQUIPO MECANICO HASTA ALCANZAR EL
NIVEL DE REFERENCIA.
- 16.-CUALQUIER MODIFICACION DEL PROYECTO SIN PREVIA CONSULTA Y
AUTORIZACION DEL CALCULISTA SERA RESPONSABILIDAD DEL PROPIETARIO
Y/O CONSTRUCTOR.
- 17.-LA NIVELACION Y ALIMENTAMIENTO DE COLUMNAS Y DEMAS ELEMENTOS
ESTRUTURALES SE HARA CON AYUDA DE LA TOPOGRAFIA.
- 18.-NINGUNA TUBERIA DE DRENAJE PODRA ATRAVESAR LOS ELEMENTOS
ESTRUTURALES DE TRABES Y COLUMNAS.
- 19.-TRASLAPES Y DORBELES NO INDICADOS SERAN DE 40% COMO MINIMO
- 20.-NO TRASLAPAR MAS DEL 50% DEL AREA DE ACERO EN UNA SOLA SECCION

TIPO DE OBRA:

PROYECTO "CITRICOLA LA VIRGEN SA DE CV".

PROPIETARIO:

CITRICOLA LA VIRGEN SA DE CV.

RESPONSABLE DE OBRA:

ARL JOSE MANUEL GUTIERREZ GARCIA

UBICACION:

CARRANZA IMPULSO LA VIRGEN DEL O
CONSTRUCCION HACIENDA LA VIRGEN.

DIR. PROJ. 1070000

PUERTO No. 000

TIPO DE PLANO:

PLANO DE FACHADAS ...

PROYECTO Y DIGITALIZO:

ARL JOSE MANUEL GUTIERREZ GARCIA

ABASTAÑADO

ARL JOSE MANUEL GUTIERREZ GARCIA

FECHA

2023/10/04

ESCALA

1:50

PLANO No.
FG-1