




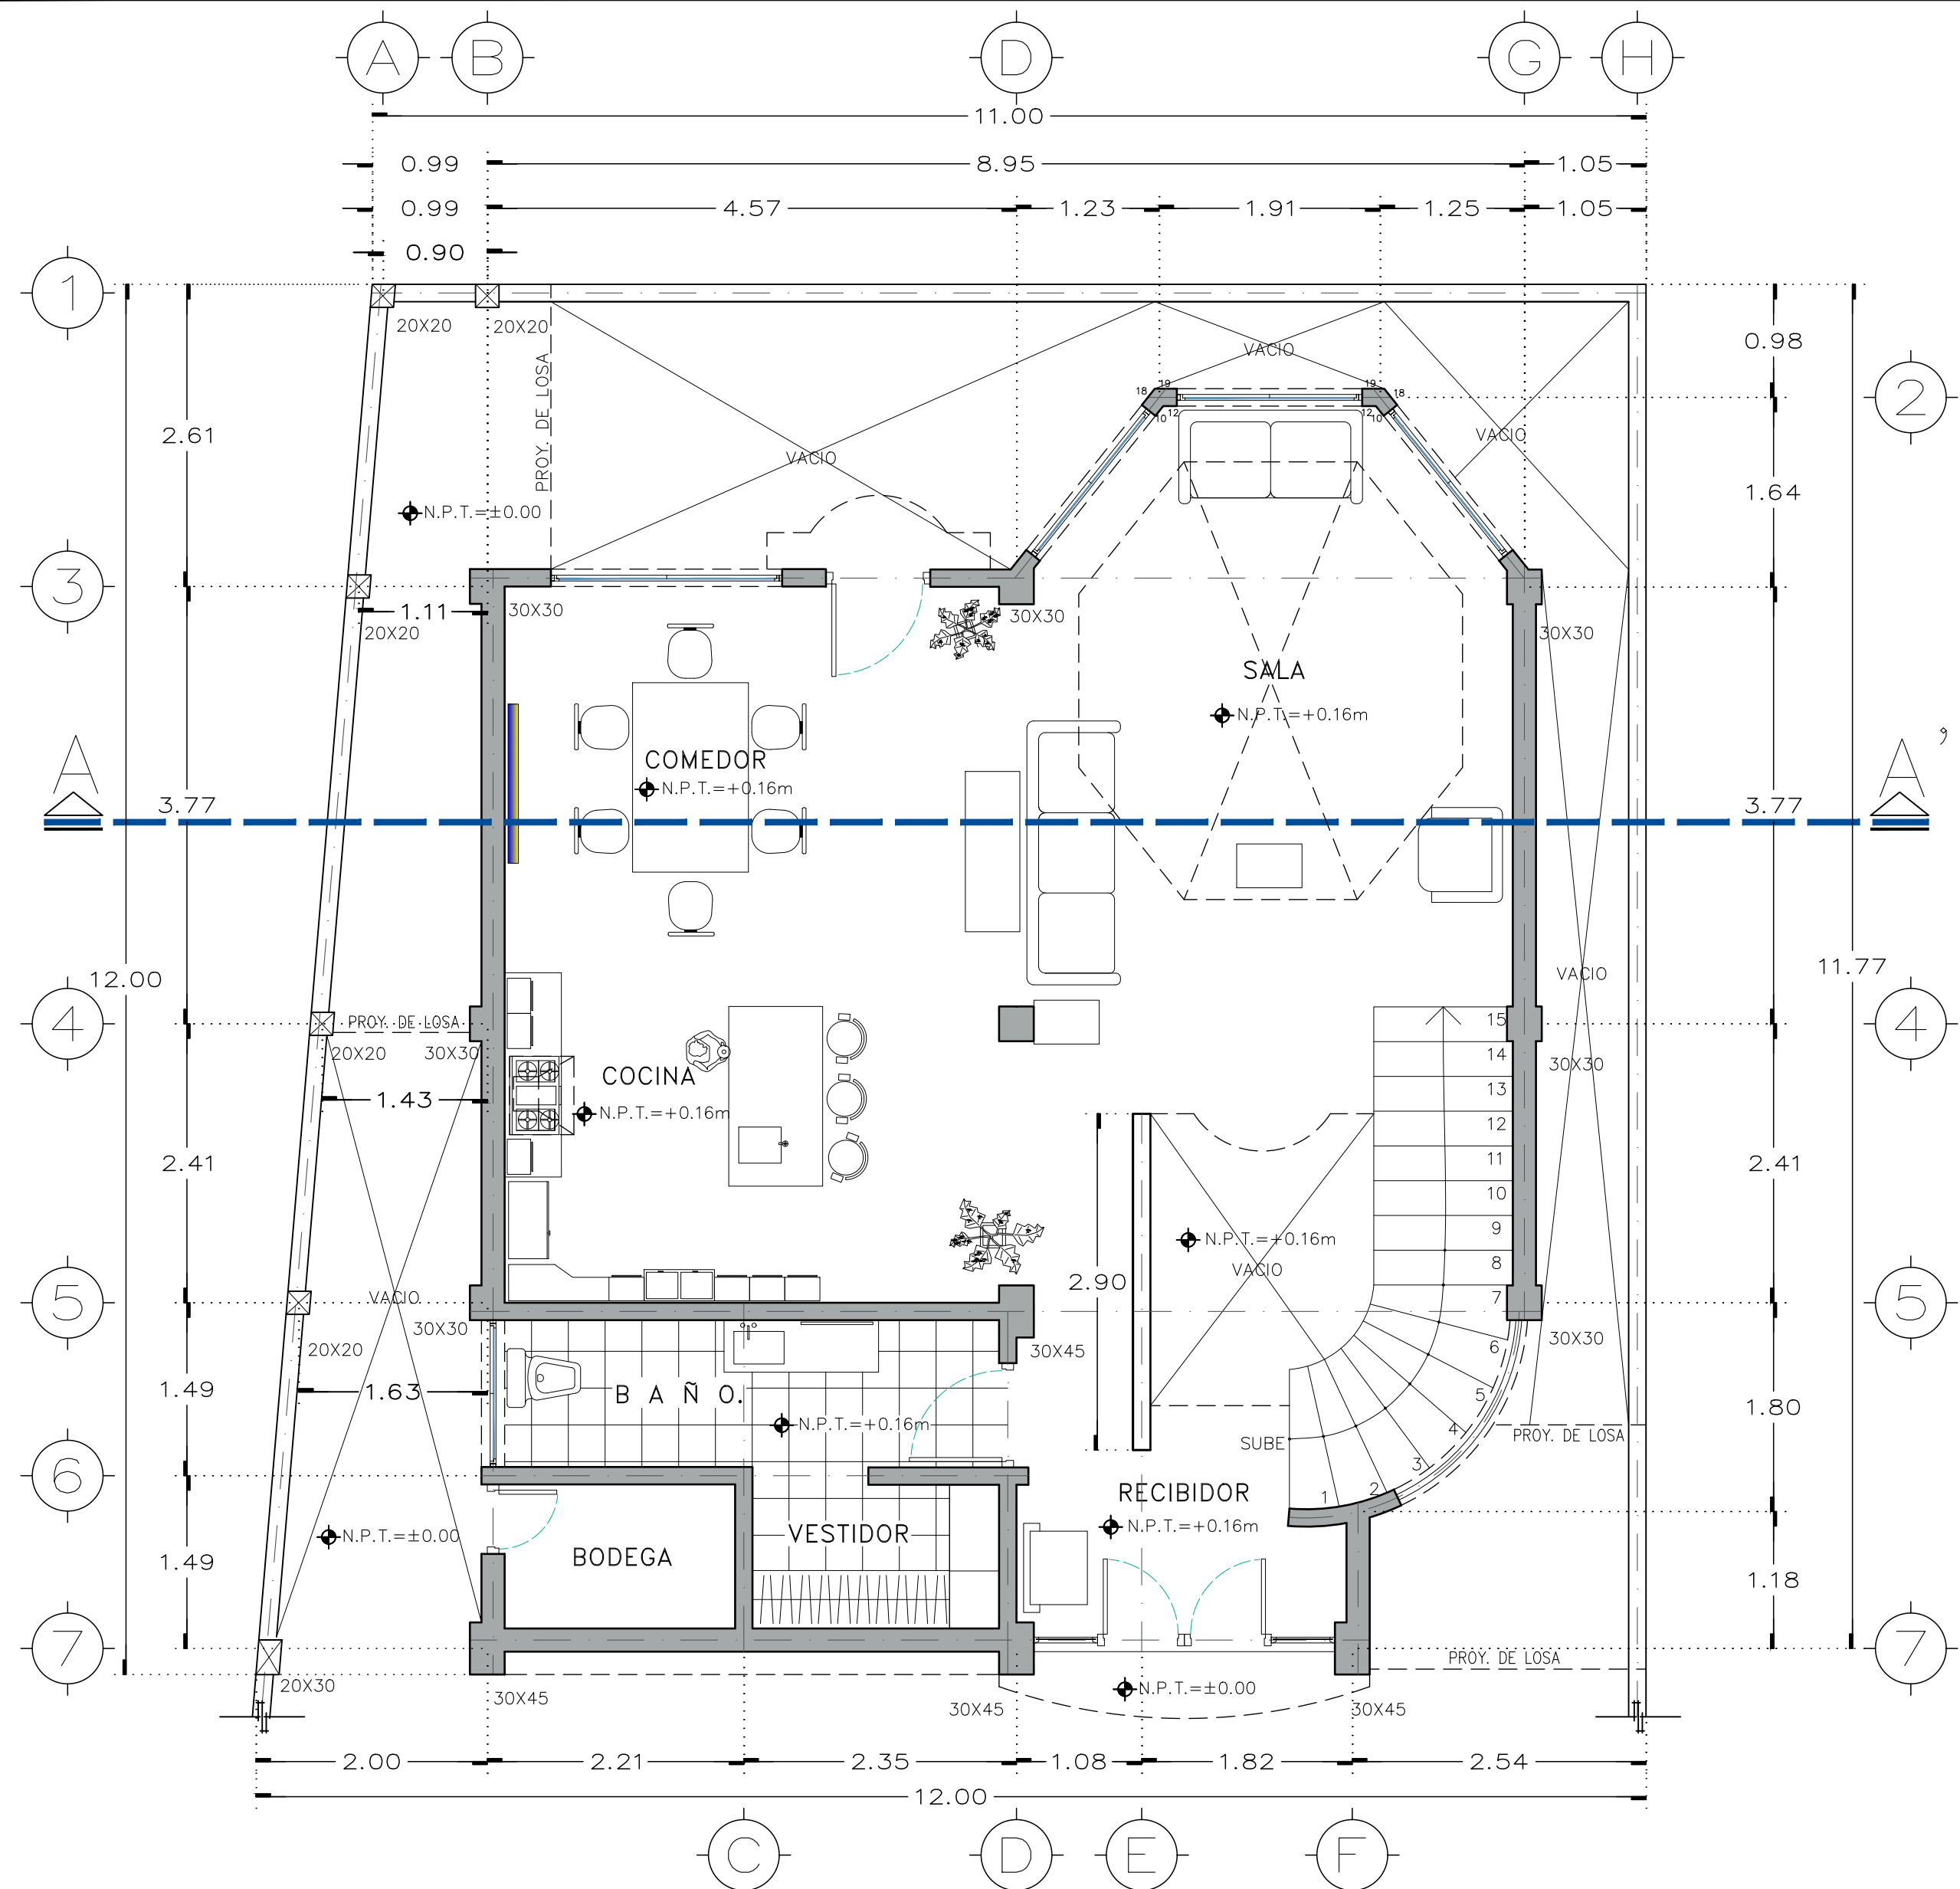


PLANTA ARQUITECTONICA BAJA
ESCALA 1:50

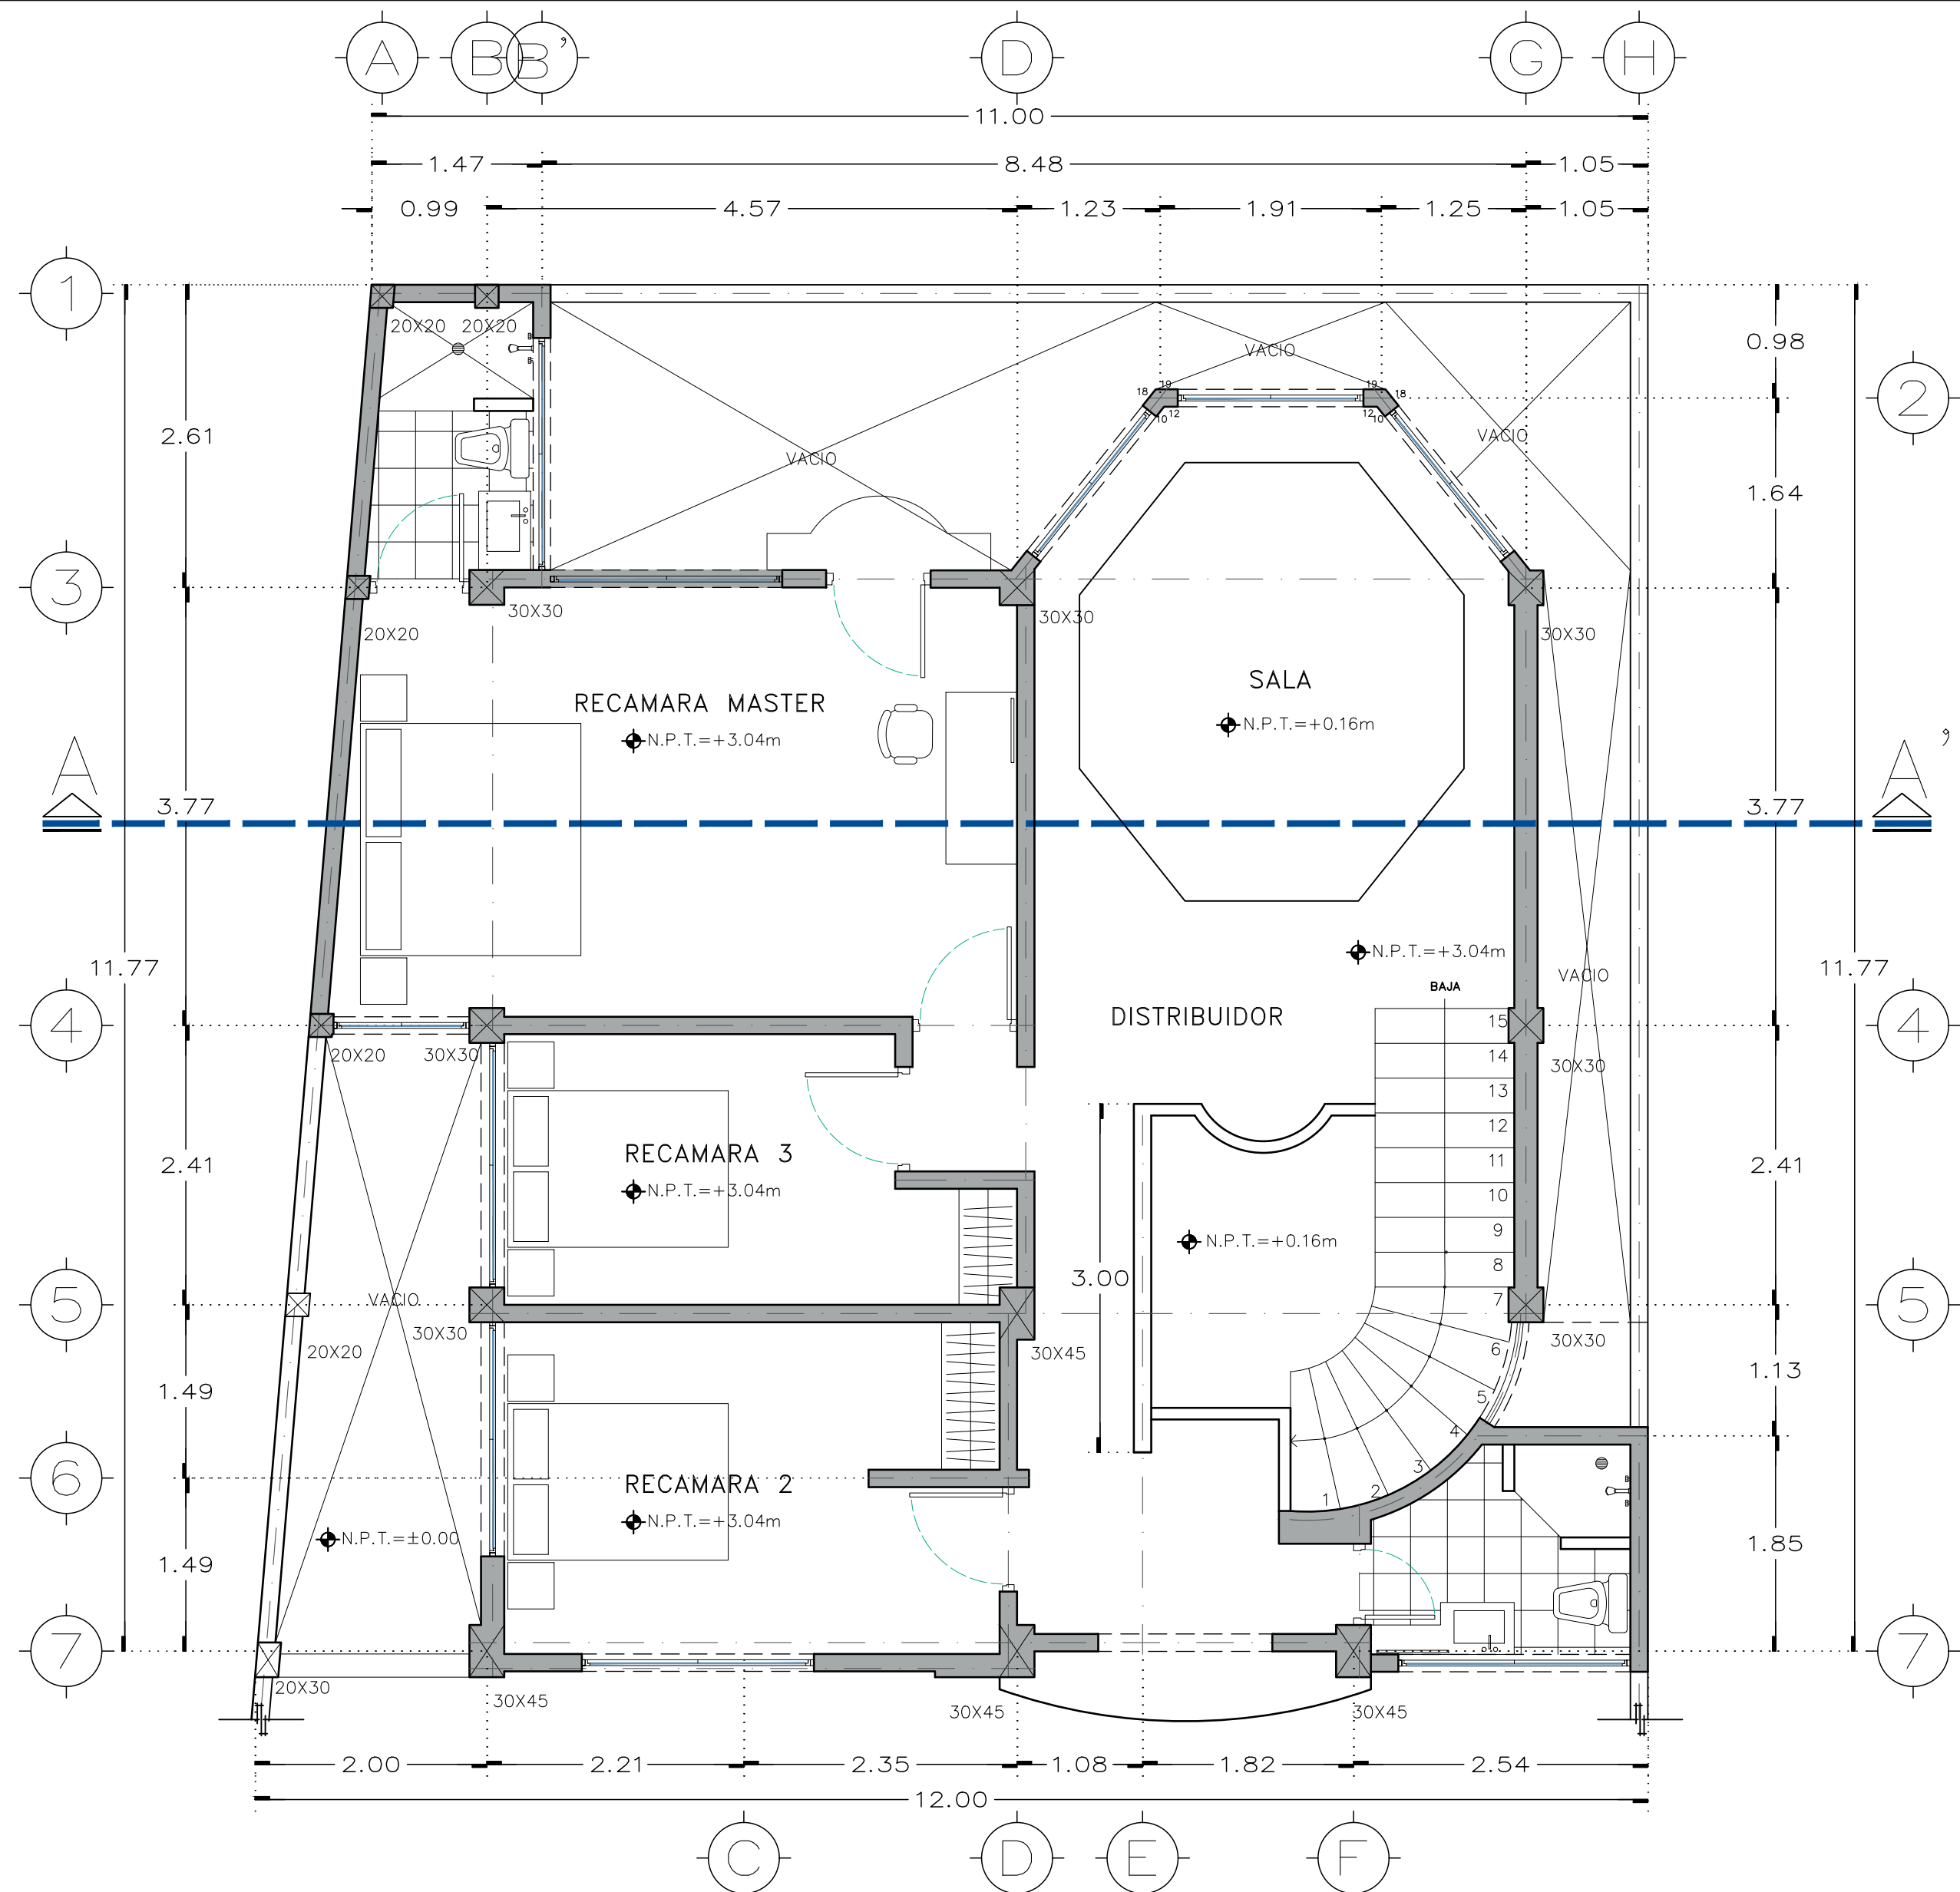


PLANTA ARQUITECTONICA ALTA
ESCALA 1:50

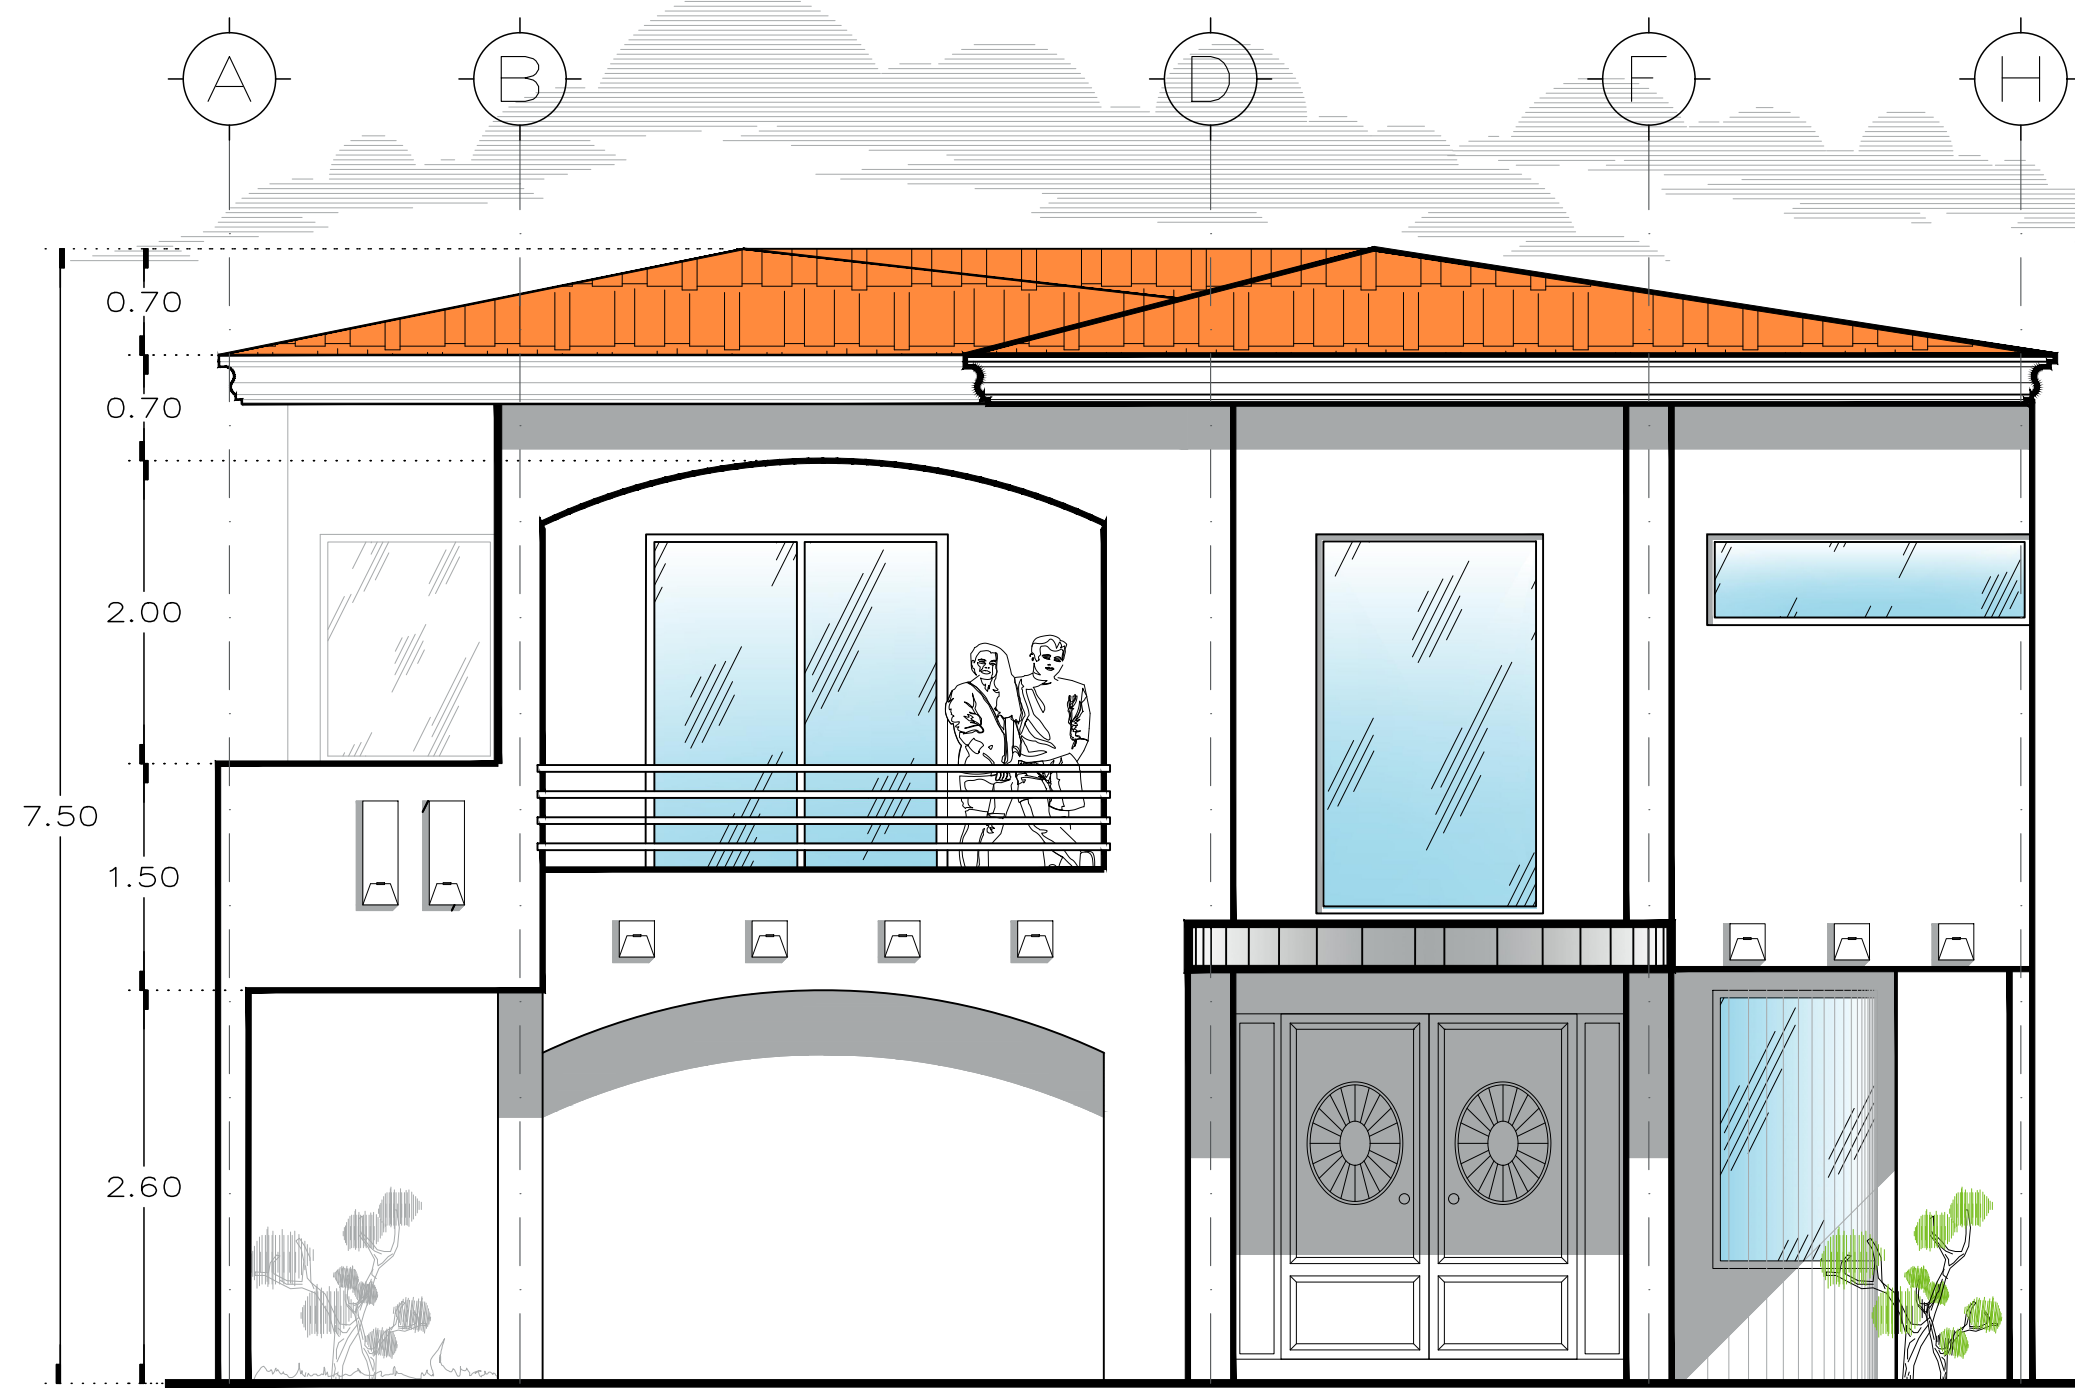

FACHADA PRINCIPAL
ESCALA 1:50

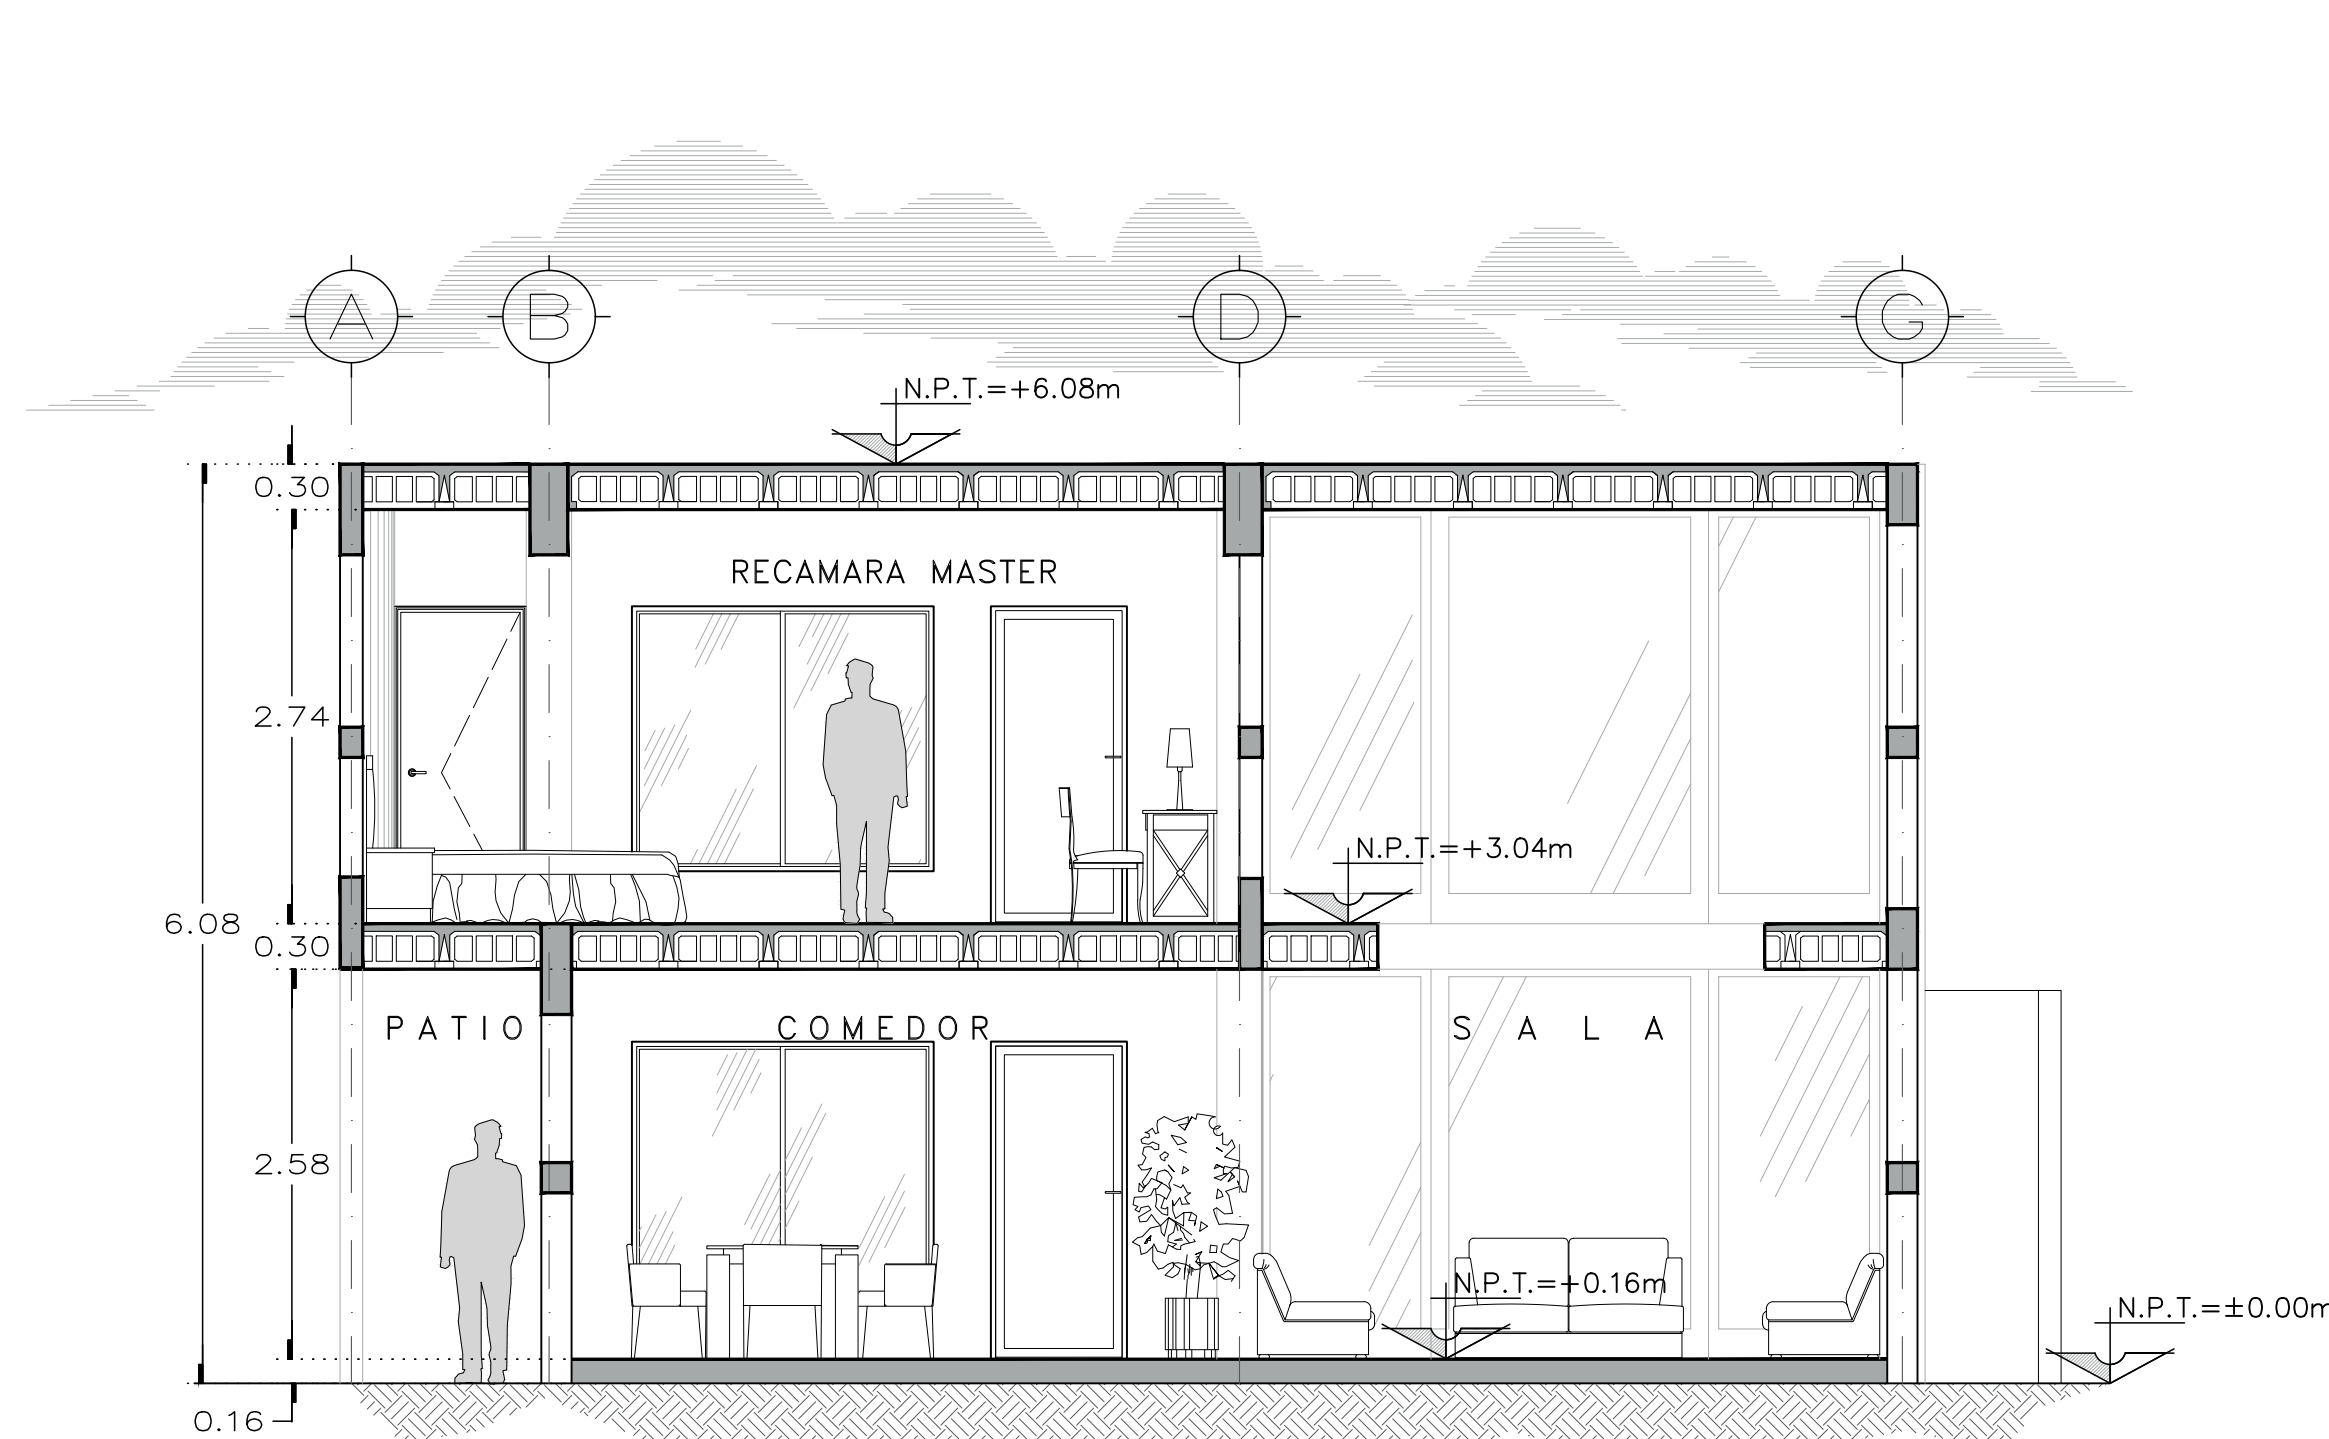

CORTE TRANSVERSAL X-X'
ESCALA 1:50

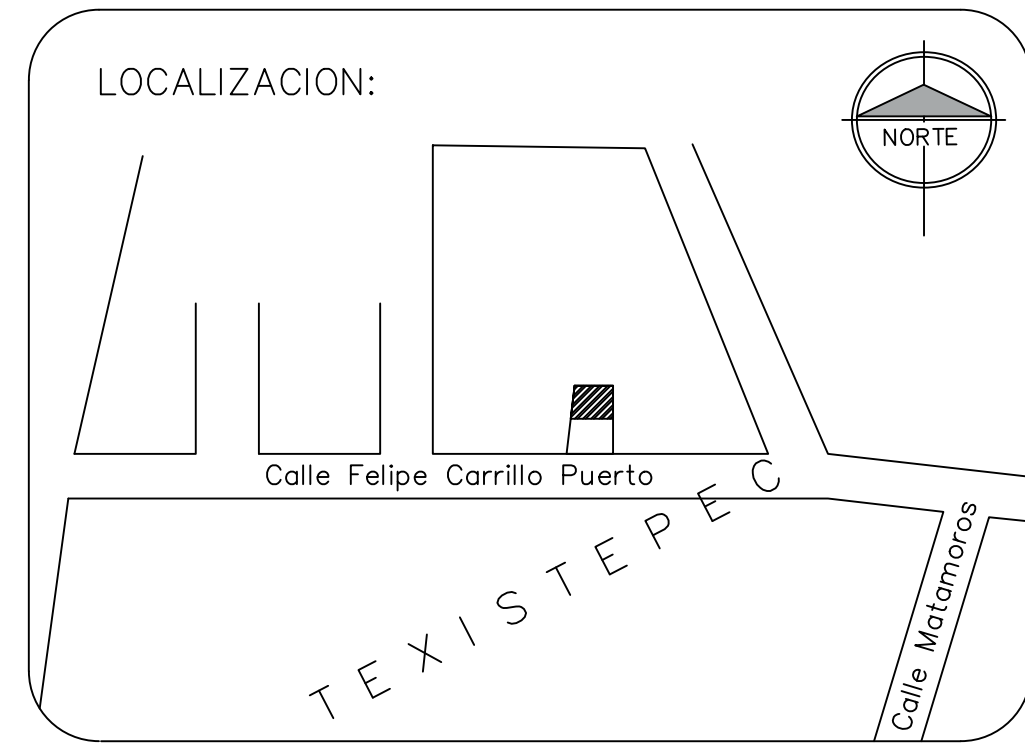

ESPECIFICACIONES ESTRUCTURALES:

CONCRETO:

- EL CONCRETO EN ZAPATAS, TRABES CADENAS, CASTILLOS Y LOSA SERÁ RESISTENCIA $F'c = 250 \text{ KG/CM}^2$ CON AGREGADO MAXIMO DE $\frac{3}{4}$ " DE ϕ .
- LOS FIRMES INTERIORES SERÁ DE CONCRETO SIMPLE CON UNA RESISTENCIA $F'c = 100 \text{ KG/CM}^2$ (PISOS).
- EL SUELO EN CIMENTACIÓN DEBERÁ ESTAR COMPACTADO AL 90% DE LA PRUEBA PROCTOR STANDARD.
- INDISPENSABLE CURAR EL CONCRETO POR CUALQUIER METODO POR 7 DIAS.
- EL RECUBRIMIENTO EN CONTACTO CON EL TERRENO NATURAL SERÁ DE 5 CMS.

ACERO:

- EL ACERO DE REFUERZO TENDRA UN LIMITE DE FLUENCIA DE $F_y = 4,200 \text{ KG/CM}^2$ EN VARS. CON UN ϕ DE $\frac{3}{8}$ ", $\frac{1}{2}$ " Y EN ARMEX $F_y = 6,000 \text{ KG/CM}^2$ Y, EN MALLA ELECTROSOLDADA $F'c = 5,000 \text{ KG/CM}^2$; NOM B-290.

INSTALACIÓN HIDRAÚLICA.

ESPECIFICACIONES:

- PARA SUMINISTROS DE AGUS EN INTERIORES Y EXTERIORES UTILIZAR TUBERIA TIPO TUBO PLUS (INTERIORES) Y (EXTERIORES).
- TODA LA TUBERIA IRA OCULTA EXCEPTO EN AZOTEA.

INSTALACIÓN SANITARIA.

ESPECIFICACIONES:

- EN INTERIORES LA TUBERIA SERÁ DE PVC. TIPO SANITARIO CON CAMPANA "ANGER" Y/O SIMILAR.
- EN EXTERIORES LA TUBERIA SERÁ DE PVC "ANGER" $\phi 100$
- LA PENDIENTE MINIMA PARA TUBERIA DE DESAGÜE DE MUEBLES Y EQUIPOS SERÁ DEL 2% PARA $\phi 8"$ Y MENORES, 1% PARA $\phi 4"$ Y MAYORES.
- TODA LA TUBERIA EXTERIOR E INTERIOR SE PROBARA CON AGUA A UNA PRESIÓN (0.30KG/CM2) MEDIDA SOBRE EL PUNTO MAS ALTO DEL TRAMO QUE SE PROBARA Y SOSTENIDA CUANDO MENOS 2 HRS.
- LA PENDIENTE GENERAL EXTERIOR ES DEL 0.6% ϕ INDICADA.
- TODOS LOS CAMBIOS DE DIRECCION SE HARÁN USANDO CONEXIONES, EVITANDO DOBLAR LAS TUBERIAS.

TODAS LAS ACOTACIONES ESTAN DADAS:

- A. LOS NIVELES EN METROS.
B. LOS DIAMETROS DE TUBERIAS EN MM.

TIPO DE OBRA:

CASA HABITACIÓN

PROPIETARIO:
C.SR. JORGE MANUEL SÁNCHEZ ORTIZ

UBICACIÓN:
CALLE FELIPE CARRILLO PUERTO No. 360,
TEXISTEPEC, VER. CP. 96180

TIPO DE PLANO:
PLANTA ARQUITECTONICA, P.A. CORTE A-A

DIGITALIZÓ:
ARQ. JOSÉ MANUEL CONTRERAS GONZÁLEZ

ACOTACIÓN:
METROS

FECHA:
MARZO / 2023

ESCALA:
1:50

CORRESPONSABLE DE OBRA:
ARQ. JOSÉ MANUEL CONTRERAS GLEZ.

CEDULA PROFESIONAL 1679326
PERITO # 017
DR SSV No 11-SSV-047/2007

PLANO No.

A-1